FLP. NO.: 1104/0041/LP/GUDA/2020/Mortgage
LP. NO.: 26/2020/1104/GUDA/DPMS

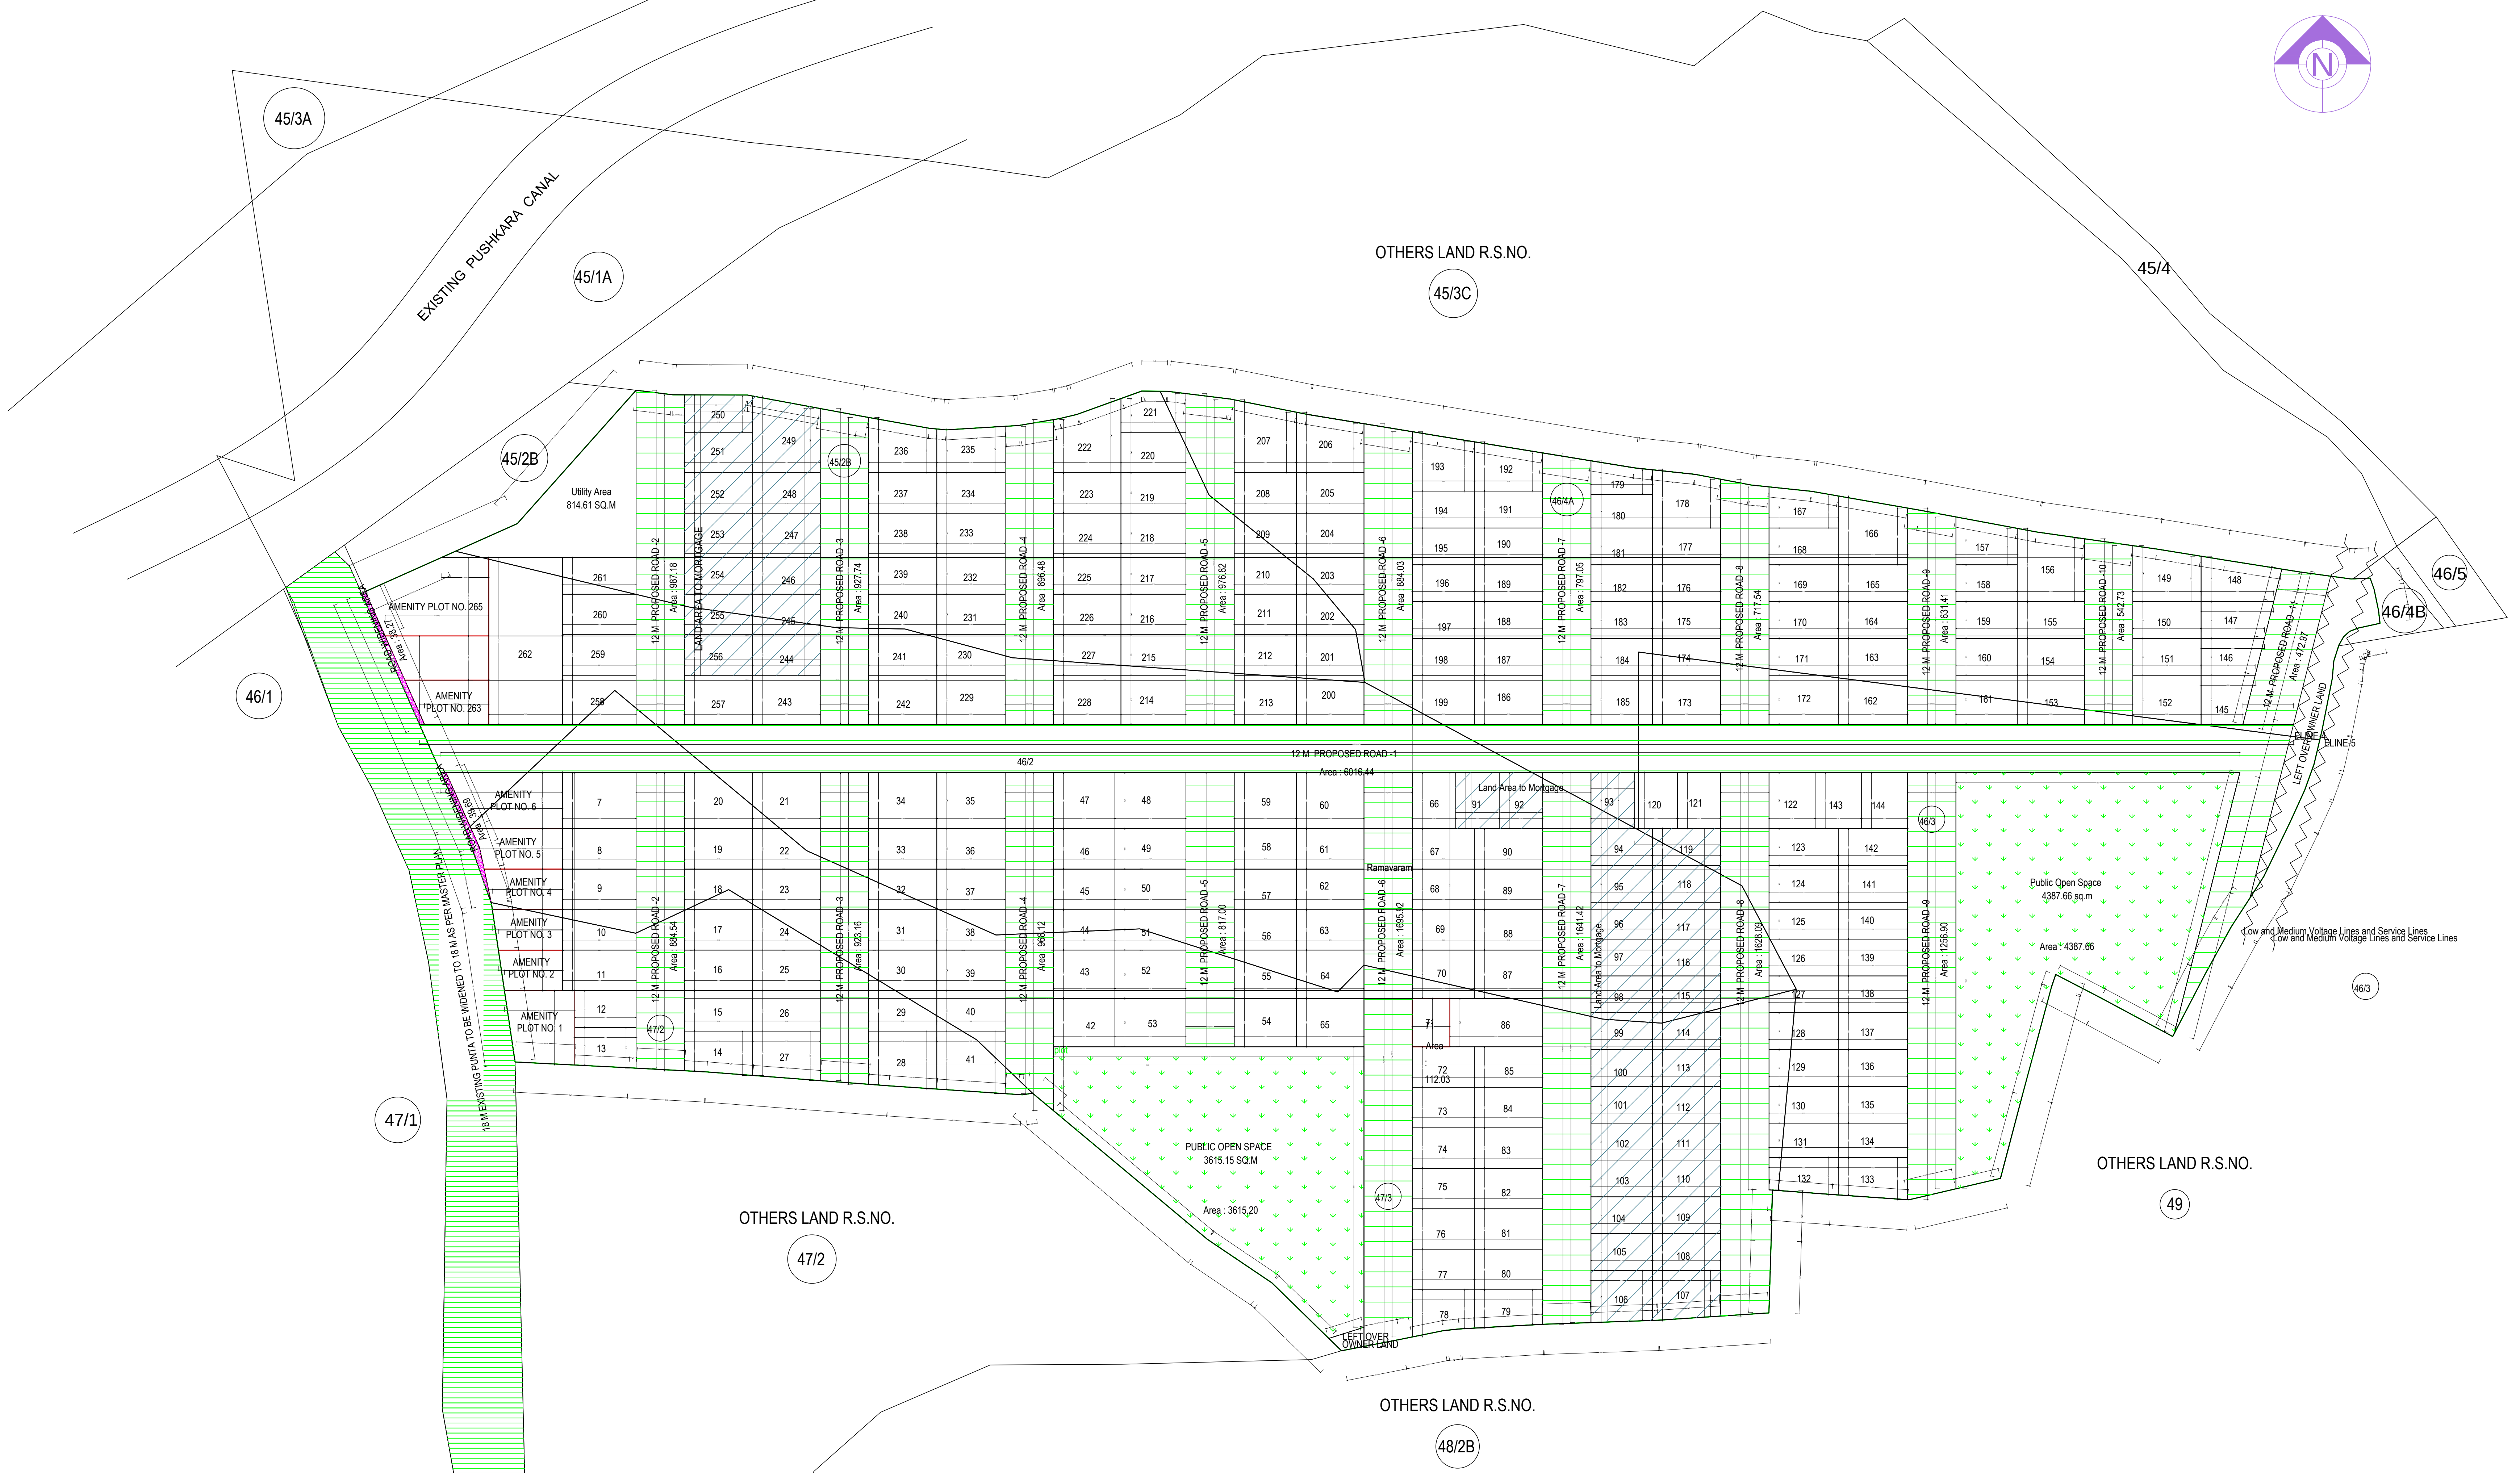

SITE PLAN

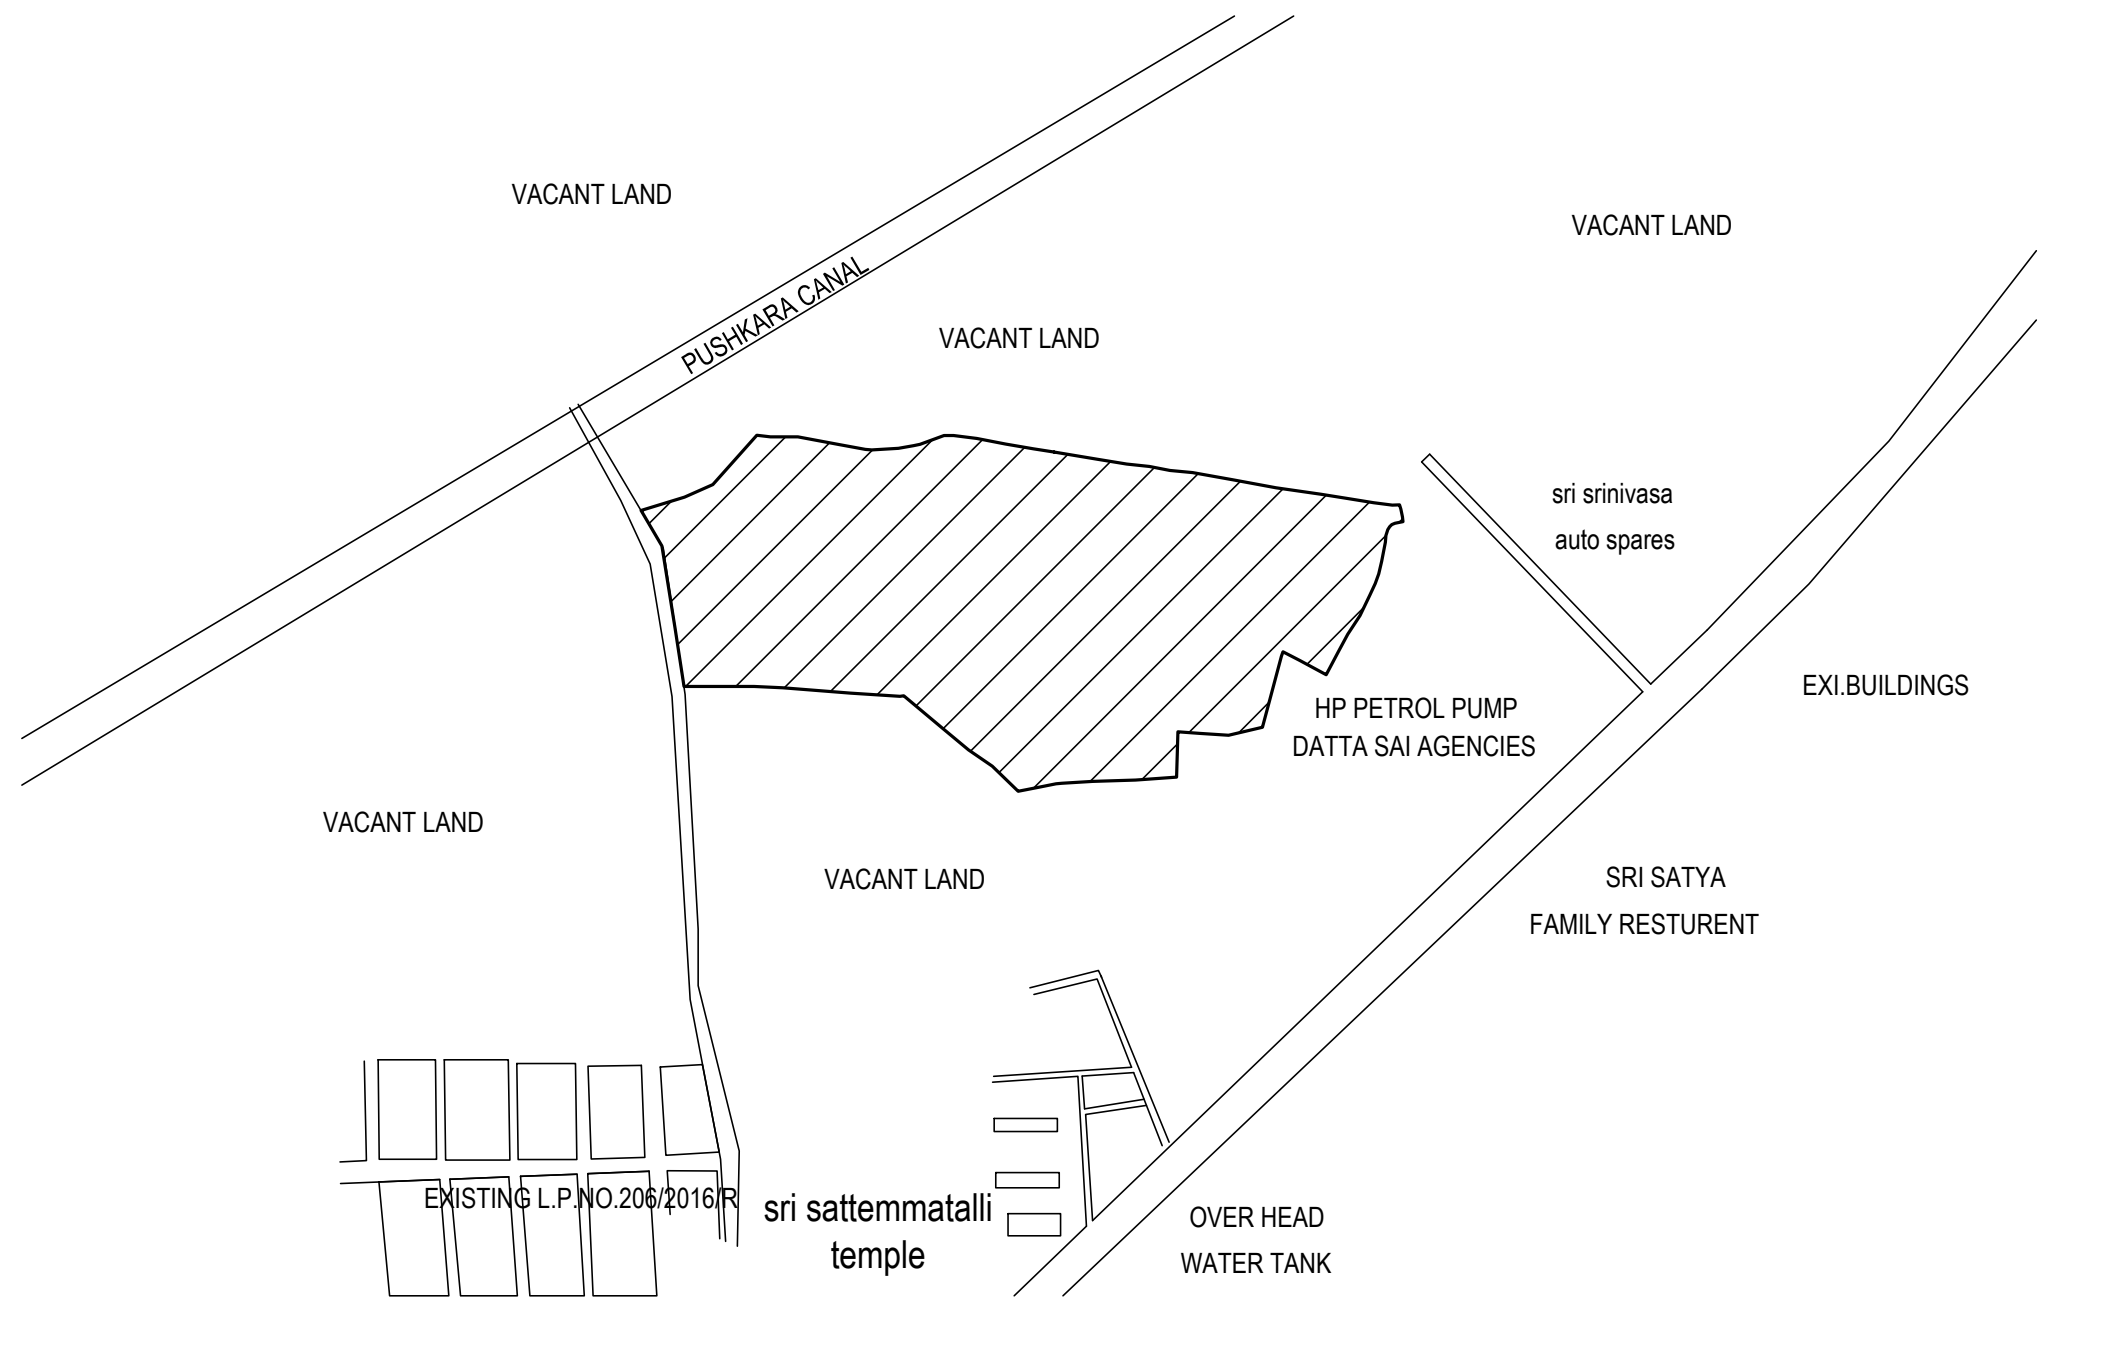

Individual Plot Area

Plot No.	Abutting Road	Plot Area		Plot Width		Plot Depth		Frontage	
		Reqd	Prop	Reqd	Prop	Reqd	Prop	Reqd	Prop
7	12 M PROPOSED ROAD -2	100.00	254.35	8.00	18.29	-	13.91	-	32.20
8	12 M PROPOSED ROAD -2	100.00	183.95	8.00	10.06	-	18.29	-	10.06
9	12 M PROPOSED ROAD -2	100.00	183.95	8.00	10.06	-	18.29	-	10.06
10	12 M PROPOSED ROAD -2	100.00	183.95	8.00	10.06	-	18.29	-	10.06
11	12 M PROPOSED ROAD -2	100.00	183.95	8.00	10.06	-	18.29	-	10.06
12	12 M PROPOSED ROAD -2	100.00	139.35	8.00	9.14	-	15.24	-	9.14
13	12 M PROPOSED ROAD -2	100.00	147.98	8.00	10.10	-	15.24	-	10.10
14	12 M PROPOSED ROAD -2	100.00	175.98	8.00	9.84	-	16.96	-	9.84
15	12 M PROPOSED ROAD -2	100.00	170.55	8.00	10.06	-	16.96	-	10.06
16	12 M PROPOSED ROAD -2	100.00	170.55	8.00	10.06	-	16.96	-	10.06
17	12 M PROPOSED ROAD -2	100.00	170.55	8.00	10.06	-	16.96	-	10.06
18	12 M PROPOSED ROAD -2	100.00	170.55	8.00	10.06	-	16.96	-	10.06
19	12 M PROPOSED ROAD -2	100.00	170.55	8.00	10.06	-	16.96	-	10.06
20	12 M PROPOSED ROAD -2	100.00	235.82	8.00	16.96	-	13.91	-	30.86
21	12 M PROPOSED ROAD -3	100.00	233.15	8.00	16.76	-	13.91	-	30.67
22	12 M PROPOSED ROAD -3	100.00	168.62	8.00	10.06	-	16.76	-	10.06
23	12 M PROPOSED ROAD -3	100.00	168.62	8.00	10.06	-	16.76	-	10.06
24	12 M PROPOSED ROAD -3	100.00	168.62	8.00	10.06	-	16.76	-	10.06
25	12 M PROPOSED ROAD -3	100.00	168.62	8.00	10.06	-	16.76	-	10.06
26	12 M PROPOSED ROAD -3	100.00	168.62	8.00	10.06	-	16.76	-	10.06
27	12 M PROPOSED ROAD -3	100.00	195.11	8.00	12.27	-	16.76	-	12.27
28	12 M PROPOSED ROAD -3	100.00	233.89	8.00	13.19	-	16.96	-	13.19
29	12 M PROPOSED ROAD -3	100.00	170.55	8.00	10.06	-	16.96	-	10.06
30	12 M PROPOSED ROAD -3	100.00	170.55	8.00	10.06	-	16.96	-	10.06
31	12 M PROPOSED ROAD -3	100.00	170.55	8.00	10.06	-	16.96	-	10.06
32	12 M PROPOSED ROAD -3	100.00	170.55	8.00	10.06	-	16.96	-	10.06
33	12 M PROPOSED ROAD -3	100.00	170.55	8.00	10.06	-	16.96	-	10.06
34	12 M PROPOSED ROAD -3	100.00	235.82	8.00	16.96	-	13.91	-	30.86
35	12 M PROPOSED ROAD -4	100.00	235.82	8.00	16.96	-	13.91	-	30.86
36	12 M PROPOSED ROAD -4	100.00	170.55	8.00	10.06	-	16.96	-	10.06
37	12 M PROPOSED ROAD -4	100.00	170.55	8.00	10.06	-	16.96	-	10.06
38	12 M PROPOSED ROAD -4	100.00	170.55	8.00	10.06	-	16.96	-	10.06
39	12 M PROPOSED ROAD -4	100.00	170.55	8.00	10.06	-	16.96	-	10.06
40	12 M PROPOSED ROAD -4	100.00	170.55	8.00	10.06	-	16.96	-	10.06
41	12 M PROPOSED ROAD -4	100.00	253.36	8.00	15.51	-	16.96	-	15.51
42	12 M PROPOSED ROAD -4	100.00	182.88	8.00	12.00	-	15.24	-	12.00
43	12 M PROPOSED ROAD -4	100.00	182.88	8.00	12.00	-	15.24	-	12.00
44	12 M PROPOSED ROAD -4	100.00	153.29	8.00	10.06	-	15.24	-	10.06
45	12 M PROPOSED ROAD -4	100.00	153.29	8.00	10.06	-	15.24	-	10.06
46	12 M PROPOSED ROAD -4	100.00	153.29	8.00	10.06	-	15.24	-	10.06
47	12 M PROPOSED ROAD -4	100.00	211.96	8.00	15.24	-	13.91	-	29.15
48	12 M PROPOSED ROAD -5	100.00	245.70	8.00	17.67	-	13.91	-	31.57
49	12 M PROPOSED ROAD -5	100.00	177.70	8.00	10.06	-	17.67	-	10.06
50	12 M PROPOSED ROAD -5	100.00	177.70	8.00	10.06	-	17.67	-	10.06
51	12 M PROPOSED ROAD -5	100.00	177.70	8.00	10.06	-	17.67	-	10.06
52	12 M PROPOSED ROAD -5	100.00	212.00	8.00	12.00	-	17.67	-	12.00
53	12 M PROPOSED ROAD -5	100.00	212.00	8.00	12.00	-	17.67	-	12.00
54	12 M PROPOSED ROAD -5	100.00	185.18	8.00	12.00	-	15.43	-	12.00
55	12 M PROPOSED ROAD -5	100.00	185.18	8.00	12.00	-	15.43	-	12.00
56	12 M PROPOSED ROAD -5	100.00	155.22	8.00	10.06	-	15.43	-	10.06
57	12 M PROPOSED ROAD -5	100.00	155.22	8.00	10.06	-	15.43	-	10.06
58	12 M PROPOSED ROAD -5	100.00	155.22	8.00	10.06	-	15.43	-	10.06
59	12 M PROPOSED ROAD -5	100.00	214.63	8.00	15.43	-	13.91	-	29.34
60	12 M PROPOSED ROAD -6	100.00	233.15	8.00	16.76	-	13.91	-	13.91
61	12 M PROPOSED ROAD -6	100.00	168.62	8.00	10.06	-	16.76	-	10.06
62	12 M PROPOSED ROAD -6	100.00	168.62	8.00	10.06	-	16.76	-	10.06
63	12 M PROPOSED ROAD -6	100.00	168.62	8.00	10.06	-	16.76	-	10.06
64	12 M PROPOSED ROAD -6	100.00	201.17	8.00	12.00	-	16.76	-	12.00
65	12 M PROPOSED ROAD -6	100.00	201.17	8.00	12.00	-	16.76	-	12.00
66	12 M PROPOSED ROAD -6	100.00	150.15	8.00	13.91	-	10.80	-	24.70
67	12 M PROPOSED ROAD -6	100.00	155.22	8.00	10.06	-	15.43	-	10.06
68	12 M PROPOSED ROAD -6	100.00	155.22	8.00	10.06	-	15.43	-	10.06
69	12 M PROPOSED ROAD -6	100.00	155.24	8.00	10.06	-	15.43	-	10.06
70	12 M PROPOSED ROAD -6	100.00	185.18	8.00	12.00	-	15.43	-	12.00
72	12 M PROPOSED ROAD -6	100.00	155.22	8.00	10.06	-	15.43	-	10.06
73	12 M PROPOSED ROAD -6	100.00	155.22	8.00	10.06	-	15.43	-	10.06
74	12 M PROPOSED ROAD -6	100.00	155.22	8.00	10.06	-	15.43	-	10.06
75	12 M PROPOSED ROAD -6	100.00	155.22	8.00	10.06	-	15.43	-	10.06
76	12 M PROPOSED ROAD -6	100.00	155.22	8.00	10.06	-	15.43	-	10.06
77	12 M PROPOSED ROAD -6	100.00	155.22	8.00	10.06	-	15.43	-	10.06
78	12 M PROPOSED ROAD -6	100.00	159.86	8.00	11.71	-	15.43	-	11.71
79	12 M PROPOSED ROAD -7	100.00	153.28	8.00	8.56	-	16.96	-	8.56
80	12 M PROPOSED ROAD -7	100.00	170.55	8.00	10.06	-	16.96	-	10.06
81	12 M PROPOSED ROAD -7	100.00	170.55	8.00	10.06	-	16.96	-	10.06
82	12 M PROPOSED ROAD -7	100.00	170.55	8.00	10.06	-	16.96	-	10.06
83	12 M PROPOSED ROAD -7	100.00	170.55	8.00	10.06	-	16.96	-	10.06
84	12 M PROPOSED ROAD -7	100.00	170.55	8.00	10.06	-	16.96	-	10.06
85	12 M PROPOSED ROAD -7	100.00	170.55	8.00	10.06	-	16.96	-	10.06
86	12 M PROPOSED ROAD -7	100.00	276.62	8.00	12.00	-	23.05	-	12.00
87	12 M PROPOSED ROAD -7	100.00	203.47	8.00	12.00	-	16.96	-	12.00
88	12 M PROPOSED ROAD -7	100.00	170.58	8.00	10.06	-	16.96	-	10.06
89	12 M PROPOSED ROAD -7	100.00	170.55	8.00	10.06	-	16.96	-	10.06
90	12 M PROPOSED ROAD -7	100.00	170.55	8.00	10.06	-	16.96	-	10.06
91	12 M PROPOSED ROAD -1	100.00	150.15	8.00	10.80	-	13.91	-	10.80
92	12 M PROPOSED ROAD -7	100.00	150.15	8.00	13.91	-	10.80	-	24.70
93	12 M PROPOSED ROAD -7	100.00	149.26	8.00	13.91	-	10.73	-	24.64
94	12 M PROPOSED ROAD -7	100.00	139.35	8.00	9.14	-	15.24	-	9.14
95	12 M PROPOSED ROAD -7	100.00	139.35	8.00	9.14	-	15.24	-	9.14
96	12 M PROPOSED ROAD -7	100.00	139.35	8.00	9.14	-	15.24	-	9.14
97	12 M PROPOSED ROAD -7	100.00	139.35	8.00	9.14	-	15.24	-	9.14
98	12 M PROPOSED ROAD -7	100.00	139.35	8.00	9.14	-	15.24	-	9.14
99	12 M PROPOSED ROAD -7	100.00	139.35	8.00	9.14	-	15.24	-	9.14
100	12 M PROPOSED ROAD -7	100.00	139.35	8.00	9.14	-	15.24	-	9.14
101	12 M PROPOSED ROAD -7	100.00	139.35	8.00	9.14	-	15.24	-	9.14
102	12 M PROPOSED ROAD -7	100.00	139.35	8.00	9.14	-	15.24	-	9.14
103	12 M PROPOSED ROAD -7	100.00	139.35	8.00	9.14	-	15.24	-	9.14
104	12 M PROPOSED ROAD -7	100.00	139.35	8.00	9.14	-	15.24	-	9.14
105	12 M PROPOSED ROAD -7	100.00	139.35	8.00	9.14	-	15.24	-	9.14
106	12 M PROPOSED ROAD -7	100.00	193.18	8.00	12.94	-	15.24	-	12.94
107	12 M PROPOSED ROAD -8	100.00	201.56	8.00	11.32	-	16.96	-	11.32
108	12 M PROPOSED ROAD -8	100.00	155.05	8.00	9.14	-	16.96	-	9.14
109	12 M PROPOSED ROAD -8	100.00	155.05	8.00	9.14	-	16.96	-	9.14
110	12 M PROPOSED ROAD -8	100.00	155.05	8.00	9.14	-	16.96	-	9.14
111	12 M PROPOSED ROAD -8	100.00	155.05	8.00	9.14	-	16.96	-	9.14
112	12 M PROPOSED ROAD -8	100.00	155.05	8.00	9.14	-	16.96	-	9.14
113	12 M PROPOSED ROAD -8	100.00	155.05	8.00	9.14	-	16.96	-	9.14
114	12 M PROPOSED ROAD -8	100.00	155.05	8.00	9.14	-	16.96	-	9.14
115	12 M PROPOSED ROAD -8	100.00	155.05	8.00	9.14	-	16.96	-	9.14
116	12 M PROPOSED ROAD -8	100.00	155.05	8.00	9.14	-	0.00	-	9.14
117	12 M PROPOSED ROAD -8	100.00	155.05	8.00	9.14	-	0.00	-	9.14
118	12 M PROPOSED ROAD -8	100.00	155.05	8.00	9.14	-	0.00	-	9.14
119	12 M PROPOSED ROAD -8	100.00	155.05	8.00	9.14	-	0.00	-	9.14
120	12 M PROPOSED ROAD -1	100.00	149.26	8.00	10.73	-	13.91	-	10.73
121	12 M PROPOSED ROAD -8	100.00	149.26	8.00	13.91	-	10.73	-	24.64
122	12 M PROPOSED ROAD -8	100.00	159.56	8.00	13.91	-	11.47	-	25.38
123	12 M PROPOSED ROAD -8	100.00	157.35	8.00	9.14	-	17.21	-	9.14
124	12 M PROPOSED ROAD -8	100.00	157.35	8.00	9.14	-	17.21	-	9.14
125	12 M PROPOSED ROAD -8	100.00	157.35	8.00	9.14	-	17.21	-	9.14
126	12 M PROPOSED ROAD -8	100.00	157.35	8.00	9.14	-	17.21	-	9.14
127	12 M PROPOSED ROAD -8	100.00	157.35	8.00	9.14	-	17.21	-	9.14
128	12 M PROPOSED ROAD -8	100.00	157.35	8.00	9.14	-	17.21	-	9.14
129	12 M PROPOSED ROAD -8	100.00	157.35	8.00	9.14	-	17.21	-	9.14
130	12 M PROPOSED ROAD -8	100.00	157.35	8.00	9.14	-	17.21	-	9.14
131	12 M PROPOSED ROAD -8	100.00	147.03	8.00	8.54	-	17.21	-	8.54
132	12 M PROPOSED ROAD -8	100.00	148.80	8.00	8.01	-	0.00	-	8.86
133	12 M PROPOSED ROAD -9	100.00	169.83	8.00	10.46	-	17.21	-	10.46
134	12 M PROPOSED ROAD -9	100.00	147.03	8.00	8.54	-	17.21	-	8.54
135	12 M PROPOSED ROAD -9	100.00	157.35	8.00	9.14	-	17.21	-	9.14
136	12 M PROPOSED ROAD -9	100.00	157.35	8.00	9.14	-	17.21	-	9.14
137	12 M PROPOSED ROAD -9	100.00	157.35	8.00	9.14	-	17.21	-	9.14
138	12 M PROPOSED ROAD -9	100.00	157.35	8.00	9.14	-	17.21	-	9.14
139	12 M PROPOSED ROAD -9	100.00	157.35	8.00	9.14	-	17.21	-	9.14
140	12 M PROPOSED ROAD -9	100.00	157.35	8.00	9.14	-	17.21	-	9.14
141	12 M PROPOSED ROAD -9	100.00	157.35	8.00	9.14	-	17.21	-	9.14
142	12 M PROPOSED ROAD -9	100.00	157.35	8.00	9.14	-	17.21	-	9.14
143	12 M PROPOSED ROAD -1	100.00	159.56	8.00	11.47	-	13.91	-	11.47
144	12 M PROPOSED ROAD -9	100.00	159.56	8.00	13.89	-	11.47	-	13.89
145	12 M PROPOSED ROAD -11	100.00	145.12	8.00	12.57	-	12.27	-	22.94
146	12 M PROPOSED ROAD -11	100.00	133.31	8.00	9.43	-	15.03	-	9.43
147	12 M PROPOSED ROAD -11	100.00	154.28	8.00	9.43	-	17.40	-	9.43
148	12 M PROPOSED ROAD -11	100.00	185.28	8.00	8.31	-	19.62	-	8.31
149	12 M PROPOSED ROAD -10	100.00	213.95	8.00	13.89	-	16.96	-	13.89
150	12 M PROPOSED ROAD -10	100.00	155.05	8.00	9.14	-	16.96	-	9.14
151	12 M PROPOSED ROAD -10	100.00	155.05	8.00	9.14	-	16.96	-	9.14
152	12 M PROPOSED ROAD -10	100.00	206.73	8.00	16.96	-	12.19	-	29.15
153	12 M PROPOSED ROAD -10	100.00	203.47	8.00	16.69	-	12.19	-	28.88
154	12 M PROPOSED ROAD -10	100.00	152.60	8.00	9.14	-	16.69	-	9.14
155	12 M PROPOSED ROAD -10	100.00	152.60	8.00	9.14	-	16.69	-	9.14
156	12 M PROPOSED ROAD -10	100.00	280.67	8.00	15.60	-	16.69	-	15.60
157	12 M PROPOSED ROAD -9	100.00	159.44	8.00	11.88	-	15.24	-	11.88
158	12 M PROPOSED ROAD -9	100.00	139.35	8.00	9.14	-	15.24	-	9.14
159	12 M PROPOSED ROAD -9	100.00	139.35	8.00	9.14	-	15.24	-	9.14
160	12 M PROPOSED ROAD -9	100.00	139.35	8.00	9.14	-	15.24	-	9.14
161	12 M PROPOSED ROAD -9	100.00	185.81	8.00	15.24	-	12.19	-	27.43
162	12 M PROPOSED ROAD -9	100.00	209.80	8.00	17.21	-	12.19	-	29.40
163	12 M PROPOSED ROAD -9	100.00	157.35	8.00	9.14	-	17.21	-	9.14
164	12 M PROPOSED ROAD -9	100.00	157.35	8.00	9.14	-	17.21	-	9.14
165	12 M PROPOSED ROAD -9	100.00	157.35	8.00	9.14	-	17.21	-	9.14
166	12 M PROPOSED ROAD -9	100.00	268.12	8.00	14.08	-	17.21	-	14.08
167	12 M PROPOSED ROAD -8	100.00	158.49	8.00	10.20	-	17.21	-	10.20
168	12 M PROPOSED ROAD -8	100.00	157.35	8.00	9.14	-	17.21	-	9.14
169	12 M PROPOSED ROAD -8	100.00	157.35	8.00	9.14	-	17.21	-	9.14
170	12 M PROPOSED ROAD -8	100.00	157.35	8.00	9.14	-	17.21	-	9.14
171	12 M PROPOSED ROAD -8	100.00	157.35	8.00	9.14	-	17.21	-	9.14
172	12 M PROPOSED ROAD -8	100.00	209.80	8.00	17.21	-	12.19	-	29.40
173	12 M PROPOSED ROAD -8	100.00	206.73	8.00	16.96	-	12.19	-	29.15
174	12 M PROPOSED ROAD -8	100.00	155.05	8.00	9.14	-	16.96	-	9.14
175	12 M PROPOSED ROAD -8	100.00	155.05	8.00	9.14	-	16.96	-	9.14
176	12 M PROPOSED ROAD -8	100.00	155.05	8.00	9.14	-	16.96	-	9.14
177	12 M PROPOSED ROAD -8	100.00	155.05	8.00	9.14	-	16.96	-	9.14
178	12 M PROPOSED ROAD -8	100.00	227.78	8.00	12.10	-	16.96	-	12.10
179	12 M PROPOSED ROAD -7	100.00	108.73	8.00	8.34	-	15.24	-	8.34
180	12 M PROPOSED ROAD -7	100.00	127.07	8.00	8.34	-	15.24	-	8.34
181	12 M PROPOSED ROAD -7	100.00	139.35	8.00	9.14	-	15.24	-	9.14
182	12 M PROPOSED ROAD -7	100.00	139.35	8.00	9.14	-	15.24	-	9.14
183	12 M PROPOSED ROAD -7	100.00	139.35	8.00	9.14	-	15.24	-	9.14
184	12 M PROPOSED ROAD -7	100.00	139.35	8.00	9.14	-	15.24	-	9.14
185	12 M PROPOSED ROAD -7	100.00	185.81	8.00	15.24	-	12.19	-	27.43
186	12 M PROPOSED ROAD -7	100.00	206.73	8.00	16.96	-	12.19	-	29.15
187	12 M PROPOSED ROAD -7	100.00	155.05	8.00	9.14	-	16.96	-	9.14
188	12 M PROPOSED ROAD -7	100.00	155.05	8.00	9.14	-	16.96	-	9.14
189	12 M PROPOSED ROAD -7	100.00	155.05	8.00	9.14	-	16.96	-	9.14
190	12 M PROPOSED ROAD -7	100.00	155.05	8.00	9.14	-	16.96	-	9.14
191	12 M PROPOSED ROAD -7	100.00	155.05	8.00	9.14	-	16.96	-	9.14
192	12 M PROPOSED ROAD -7	100.00	184.26	8.00	9.48	-	16.96	-	9.48
193	12 M PROPOSED ROAD -6	100.00	208.46	8.00	14.77	-	15.43	-	14.77
194	12 M PROPOSED ROAD -6	100.00	141.11	8.00	9.14	-	15.43	-	9.14
195	12 M PROPOSED ROAD -6	100.00	141.11	8.00	9.14	-	15.43	-	9.14
196	12 M PROPOSED ROAD -6	100.00	141.11	8.00	9.14	-	15.43	-	9.14
197	12 M PROPOSED ROAD -6	100.00	141.11	8.00	9.14	-	15.43	-	9.14
198	12 M PROPOSED ROAD -6	100.00	141.11	8.00	9.14	-	15.43	-	9.14
199	12 M PROPOSED ROAD -6	100.00	188.15	8.00	15.43	-	12.19	-	27.62
200	12 M PROPOSED ROAD -6	100.00	204.39	8.00	16.76	-	12.19	-	28.96
201	12 M PROPOSED ROAD -6	100.00	168.62	8.00	10.06	-	16.76	-	10.06
202	12 M PROPOSED ROAD -6	100.00	168.62	8.00	10.06	-	16.76	-	10.06
203	12 M PROPOSED ROAD -6	100.00	168.62	8.00	10.06	-	16.76	-	10.06
204	12 M PROPOSED ROAD -6	100.00	168.62	8.00	10.06	-	16.76	-	10.06
205	12 M PROPOSED ROAD -6	100.00	168.62	8.00	10.06	-	16.76	-	10.06
206	12 M PROPOSED ROAD -6	100.00	227.23	8.00	12.17	-	16.76	-	12.17
207	12 M PROPOSED ROAD -5	100.00	255.60	8.00	18.11	-	15.43	-	18.11
208	12 M PROPOSED ROAD -5	100.00	155.22	8.00	10.06	-	15.43	-	10.06
209	12 M PROPOSED ROAD -5	100.00	155.22	8.00	10.06	-	15.43	-	10.06
210	12 M PROPOSED ROAD -5	100.00	155.22	8.00	10.06	-	15.43	-	10.06
211	12 M PROPOSED ROAD -5	100.00	155.22	8.00	10.06	-	15.43	-	10.06
212	12 M PROPOSED ROAD -5	100.00	155.22	8.00	10.06	-	15.43	-	10.06
213	12 M PROPOSED ROAD -5	100.00	188.15	8.00	15.43	-	12.19	-	27.62
214	12 M PROPOSED ROAD -5	100.00	196.81	8.00	16.14	-	12.19	-	28.33
215	12 M PROPOSED ROAD -5	100.00	162.37	8.00	10.06	-	16.14	-	10.06
216	12 M PROPOSED ROAD -5	100.00	162.37	8.00	10.06	-	16.14	-	10.06
217	12 M PROPOSED ROAD -5	100.00	162.37	8.00	10.06	-	16.14	-	10.06
218	12 M PROPOSED ROAD -5	100.00	162.37	8.00	10.06	-	16.14	-	10.06
219	12 M PROPOSED ROAD -5	100.00	162.37	8.00	10.06	-	16.14	-	10.06
220	12 M PROPOSED ROAD -5	100.00	162.37	8.00	10.06	-	16.14	-	10.06
221	12 M PROPOSED ROAD -5	100.00	158.36	8.00	9.60	-	16.14	-	9.60
222	12 M PROPOSED ROAD -4	100.00	260.13	8.00	13.19	-	16.76	-	13.19
223	12 M PROPOSED ROAD -4	100.00	168.62	8.00	10.06	-	16.76	-	10.06
224	12 M PROPOSED ROAD -4	100.00	168.62	8.00	10.06	-	16.76	-	10.06
225	12 M PROPOSED ROAD -4	100.00	168.62	8.00	10.06	-	16.76	-	10.06
226	12 M PROPOSED ROAD -4	100.00	168.62	8.00	10.06	-	16.76	-	10.06
227	12 M PROPOSED ROAD -4	100.00	168.62	8.00	10.06	-	16.76	-	10.06
228	12 M PROPOSED ROAD -4	100.00	204.39	8.00	16.76	-	12.19	-	28.96
229	12 M PROPOSED ROAD -4	100.00	206.73	8.00	16.96	-	12.19	-	29.15
230	12 M PROPOSED ROAD -4	100.00	170.55	8.00	10.06	-	16.96	-	10.06
231	12 M PROPOSED ROAD -4	100.00	170.55	8.00	10.06	-	16.96	-	10.06
232	12 M PROPOSED ROAD -4	100.00	170.55	8.00	10.06	-	16.96	-	10.06
233	12 M PROPOSED ROAD -4	100.00	170.55	8.00	10.06	-	16.96	-	10.06
234	12 M PROPOSED ROAD -4	100.00	170.55	8.00	10.06	-	16.96	-	10.06
235	12 M PROPOSED ROAD -4	100.00	187.32	8.00	11.53	-	16.96	-	11.53
236	12 M PROPOSED ROAD -3	100.00	207.28	8.00	13.73	-	16.96	-	13.73
237	12 M PROPOSED ROAD -3	100.00	170.55	8.00	10.06	-	16.96	-	10.06
238	12 M PROPOSED ROAD -3	100.00	170.55	8.00	10.06	-	16.96	-	10.06
239	12 M PROPOSED ROAD -3	100.00	170.55	8.00	10.06	-	16.96	-	10.06
240	12 M PROPOSED ROAD -3	100.00	170.55	8.00	10.06	-	16.96	-	10.06
241	12 M PROPOSED ROAD -3	100.00	170.55	8.00	10.06	-	16.96	-	10.06
242	12 M PROPOSED ROAD -3	100.00	206.73	8.00	16.96	-	12.19	-	29.15
243	12 M PROPOSED ROAD -3	100.00	204.39	8.00	16.76	-	12.19	-	28.96
244	12 M PROPOSED ROAD -3	100.00	168.62	8.00	10.06	-	16.76	-	10.06
245	12 M PROPOSED ROAD -3	100.00	168.62	8.00	10.06	-	16.76	-	10.06
246	12 M PROPOSED ROAD -3	100.00	168.62	8.00	10.06	-	16.76	-	10.06
247	12 M PROPOSED ROAD -3	100.00	168.62	8.00	10.06	-	16.76	-	10.06
248	12 M PROPOSED ROAD -3	100.00	168.62	8.00	10.06	-	16.76	-	10.06
249	12 M PROPOSED ROAD -3	100.00	293.32	8.00	15.94	-	16.76	-	15.94
250	12 M PROPOSED ROAD -2	100.00	156.84	8.00	9.29	-	16.96	-	9.29
251	12 M PROPOSED ROAD -2	100.00	170.55	8.00	10.06	-	16.96	-	10.06
252	12 M PROPOSED ROAD -2	100.00	170.55	8.00	10.06	-	16.96	-	10.06
253	12 M PROPOSED ROAD -2	100.00	170.55	8.00	10.06	-	16.96	-	10.06
254	12 M PROPOSED ROAD -2	100.00	170.55	8.00	10.06	-	16.96	-	10.06
255	12 M PROPOSED ROAD -2	100.00	170.55	8.00	10.06	-	16.96	-	10.06
256	12 M PROPOSED ROAD -2	100.00	170.55	8.00	10.06	-	16.96	-	10.06
257	12 M PROPOSED ROAD -2	100.00	206.73	8.00	16.96	-	12.19	-	29.15
258	12 M PROPOSED ROAD -2	100.00	222.97	8.00	18.29	-	12.19	-	30.48
259	12 M PROPOSED ROAD -2	100.00	183.95	8.00	10.06	-	18.29	-	10.06
260	12 M PROPOSED ROAD -2	100.00	183.95	8.00	10.06	-	18.29	-	10.06
261	12 M PROPOSED ROAD -2	100.00	167.23	8.00	9.14	-	18.29	-	9.14
262	12 M PROPOSED ROAD -1	100.00	758.09	8.00	18.29	-	41.45	-	18.29

TLP NO:1104/0041/LP/GUDA/2020	SHEET NO.	1	DATE	02-11-2020

Project Title :Project Title :PLAN SHOWING THE PROPOSED LAYOUT FOR HOUSE PLOTS IN R. S.NO : 45/2B,46/2,3,4A,47/2 & 3 OF RAMAVARAM VILLAGE & GRAMPANCHAYAT , JAGGAMPETA MANDAL , E.G.DIST.BELONGS TO: 1) SRI PENMASTHA VENKATA RAMAKRISHNAM RAJU, S/O P. KRISHNAM RAJU , 2) SMT VETUKURI PUSHPAVATHI, W/O KRISHNAM RAJU, 3) SRI CHEKURI SIVARAMA RAJU, S/O CH.KRISHNAM RAJU,4) SRI VETUKURI KRISHNAM RAJU, S/O.V.VENKATRAJU, 5) SMT. CHEKURI BHAGYA SUNDHARAM, W/O. CH. SIVARAMA RAJU, DEVELOPER: MUDUNURI MURALI KRISHNAMRAJU, S/O.M.RAMARAJU

AREA STATEMENT	VERSION NO.: 1.101.96	
	VERSION DATE: 27/10/2020	
PROJECT DETAIL:		
Region: RAJAHMUNDRY REGION	Plot Use: Residential	
Authority: GODAVARI URBAN DEVELOPMENT AUTHORITY	Land Use Zone: Residential use Zone	
TLP No.: 1104/0041/LP/GUDA/2020	Main Abutting Road Width: 18	
Application Type: General Proposal	If Plot is abutting to Highway: No	
Project Type: Open Layout	Plot No: NA	
Nature of Development: Revision	Survey No.: 45/2B,46/2,3,4A,47/2 & 3	
Location: GP under GUDA	North: -	
SubLocation: NA	South: -	
Village Name: Ramavaram	East: -	
Mandal: JAPMDL	West: -	
AREA DETAILS:		SQ.MT.
AREA OF PLOT (Minimum)	(A)	79860.94
Deduction for NetPlot Area		
LeftOverOwnerLand Area		578.43
Total		578.43
NET AREA OF PLOT	(A-Deductions)	79282.51
Deduction for Balance Plot Area		
Road Widening Area		77.97
Amenity Area		2425.85
LeftOverOwnerLand Area		578.43
Total		3082.25
BALANCE AREA OF PLOT	(A-Deductions)	76778.69

Land use analysis/Area distribution (Table 2c)

Area covered under	Proposed Area in sq. mt.	Proposed Area in sq. yd.	Percentage(%)
Plotted Area	44295.46	52976.93	55.47
Leftover Owners Land Area	578.43	691.80	0.72
Road Area	23743.52	28397.01	29.73
AMENITY PLOT NO. 6	358.87	429.21	0.45
AMENITY PLOT NO. 4	185.15	221.44	0.23
AMENITY PLOT NO. 1	291.50	348.63	0.37
AMENITY PLOT NO. 265	490.93	587.15	0.61
AMENITY PLOT NO. 263	202.14	241.76	0.25
AMENITY PLOT NO. 5	209.14	250.13	0.26
71	112.03	133.99	0.14
AMENITY PLOT NO. 264	255.88	306.02	0.32
AMENITY PLOT NO. 3	167.66	200.52	0.21
AMENITY PLOT NO. 2	152.54	182.44	0.19
Public Open Space	8002.86	9571.34	10.02
Utility Area	814.61	974.27	1.02
Total net layout	79860.73	95512.63	100.00

LTP NAME AND SIGNATURE	STRUCTURAL ENG NAME AND SIGNATURE	BUILDER NAME AND SIGNATURE
Kammula V.Rama Krishna		MUDUNURY MURALI KRISHNAMRAJU
21/2017/SE/GUDA		REG/1104/0094/2020

Mortgage Area Details

Name	Mortgage Area	
	Reqd	Prop
Land Area to Mortgage	6644.32	6693.66

Land Area to Mortgage Details

Name	Ind Plot Name	Ind Plot Area
LAND AREA TO MORTGAGE	244	168.62
	245	168.62
	246	168.62
	247	168.62
	248	168.62
	249	293.32
	250	156.84
	251	170.55
	252	170.55
	253	170.55
	254	170.55
	255	170.55
	256	170.55
Land Area to Mortgage	93	149.26
	94	139.35
	95	139.35
	96	139.35
	97	139.35
	98	139.35
	99	139.35
	100	139.35
	101	139.35
	102	139.35
	103	139.35
	104	139.35
	105	139.35
	106	193.18
	107	201.56
	108	155.05
	109	155.05
	110	155.05
	111	155.05
	112	155.05
	113	155.05
	114	155.05
	115	155.05
	116	155.05
	117	155.05
	118	155.05
	119	155.05
Land Area to Mortgage	91	150.15
	92	150.15
Total	-	6693.66

General Conditions

No.	General Conditions
1	LTP is responsible for any misrepresentation in above aspects.
2	Splay shall be maintained as per GO.MS NO.119. MA & UD dt 27.03.2017 in all the road corners.

COLOR INDEX	
Plot / Site lines	—
Existing street / road	🟩
Proposed work including servicies	🟥
Existing construction proposed to be demolished	▨
Existing structure to be retained	▨
Work in progress duly sanctioned	—
Open Space	☐
Drainage and Sewerage work	▨
Water Supply work	▨
Deviations	▨
Recreation ground	▨

ISO_full_bleed_2A0_(1189.00_x_1682.00_MM)

This is system generated report and does not require any signature.For further confirmation you can access the department website www.apdpms.ap.gov.in with file number.
Accuracy of Scrutiny Report and Drawing is subject to accuracy of end-user provided data, 3rd party software/hardware/services, etc. We are not liable for any damages which may arise from use, or inability to use the Application.